
 


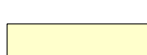


- | | | | |
|---|-------------------|---|--------------------|
|  | - Конференц-зал |  | - Санузлы М/Ж |
|  | - Open workspace |  | - Входная зона |
|  | - Переговорная |  | - Гардероб |
|  | - Офис |  | - Кафетерий |
|  | - Учебная комната |  | - Prayer room |
|  | - Коридор |  | - Бум |
|  | - Зона отдыха |  | - Раздевальная М/Ж |
|  | - Phone booth |  | - Душевая М/Ж |
|  | - Кладовая |  | - Meeting room |

Условные обозначения

① -марка помещения (номер)

Функциональное зонирование	Примечания 1. Высота потолка h=3370 мм. 2. Все размеры даны в миллиметрах. 3. Все привязки даны к стенам в черновой отделке. 4. После демонтажа и монтажа стен размеры могут изменяться. 5. Необходимо учитывать возможные погрешности в проектных и реальных размерах. 6. Высотные отметки даны от цоколя чистового пола 0.000.	Изм. №	Описание	Подпись	Наименование проекта	№ проекта	Дата	Масштаб	№ листа
					Дизайн проект - АИ	Дизайн проект - АИ	03.07.2026 12:50:08	Как указано	9

План расстановки мебели
М 1 : 100

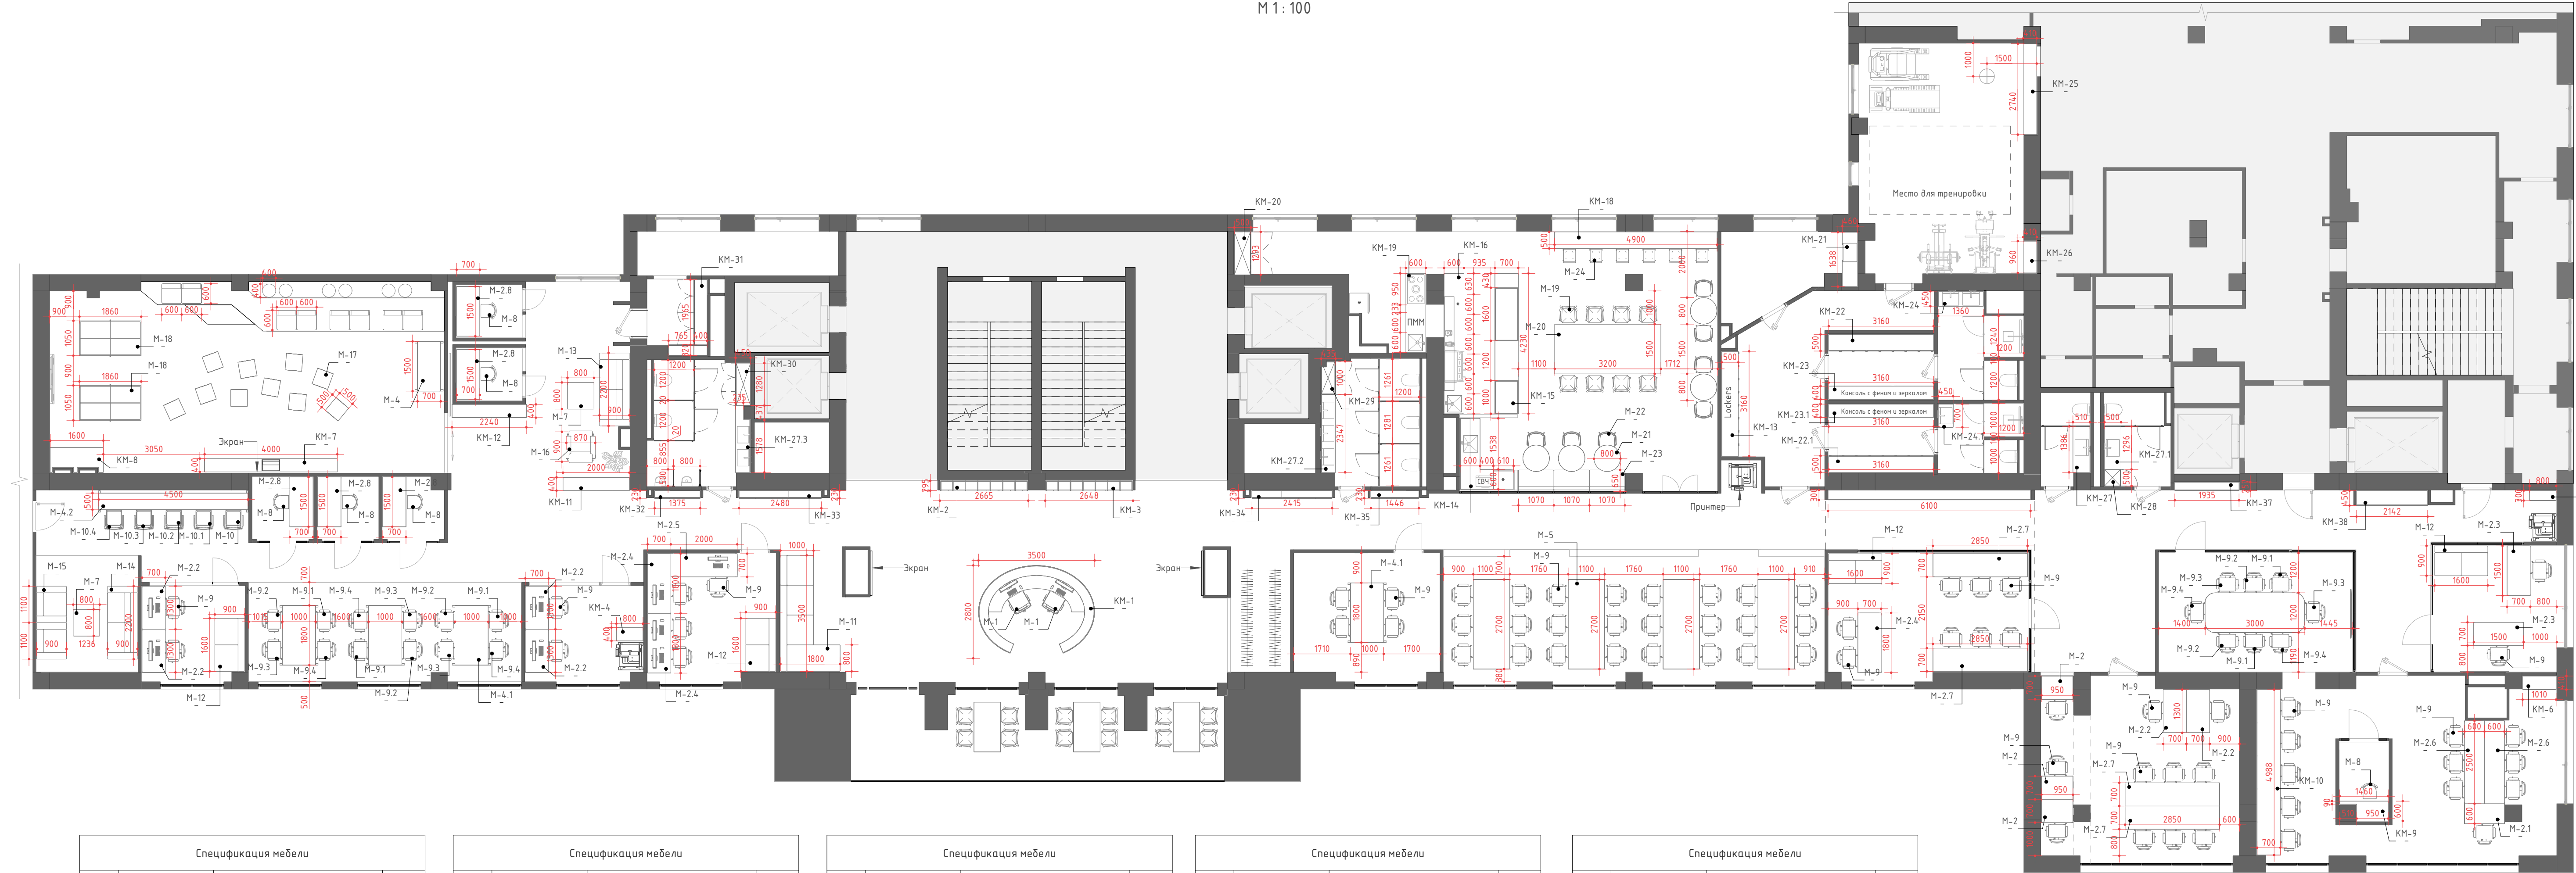

Спецификация мебели			
Поз.	Изображение	Описание	Кол-во
М-1		Рабочее кресло	2
М-2		Стол письменный. Размеры: 950х700х750h	3
М-2.1		Стол письменный. Размеры: 1200х600х750h	1
М-2.2		Стол письменный. Размеры: 1300х700х750h	6
М-2.3		Стол письменный. Размеры: 1500х700х750h	2
М-2.4		Стол письменный. Размеры: 1800х700х750h	3
М-2.5		Стол письменный. Размеры: 2000х700х750h	1
М-2.6		Стол письменный. Размеры: 2500х600х750h	2
М-2.7		Стол письменный. Размеры: 2850х700х750h	4
М-2.8		Стол письменный. Размеры: 1500х700х1000h	5

Спецификация мебели			
Поз.	Изображение	Описание	Кол-во
М-3		Тумбочка для письменного стола	20
М-4		Стол прямоугольный. Размеры: 1500х700х750h	1
М-4.1		Стол прямоугольный. Размеры: 1800х1000х750h	4
М-4.2		Стол прямоугольный. Размеры: 4500х500х750h	1
М-5		Стол прямоугольный. Размеры: 2700х1100х750h	4
М-6		Стол. Размеры: 3000х1200х750h	1
М-7		Журнальный стол. Размеры: 800х800х400h	2
М-8		Стул барный	6
М-9		Рабочее кресло	69
М-9.1		Рабочее кресло	5
М-9.2		Рабочее кресло	5

Спецификация мебели			
Поз.	Изображение	Описание	Кол-во
М-9.3		Рабочее кресло	5
М-9.4		Рабочее кресло	5
М-10		Рабочее кресло	1
М-10.1		Рабочее кресло	1
М-10.2		Рабочее кресло	1
М-10.3		Рабочее кресло	1
М-10.4		Рабочее кресло	1
М-11		Диван модульный. Размеры: 3500х1800х420mm	1
М-12		Диван модульный. Размеры: 1600х900х420mm	4
М-13		Диван. Размеры: 2200х900х420mm	1

Спецификация мебели			
Поз.	Изображение	Описание	Кол-во
М-14		Диван. Размеры: 2200х900х420mm	1
М-15		Кресло. Размеры: 1100х900х420mm	2
М-16		Кресло. Размеры: 870х900х420mm	1
М-17		Пуф-трансформер. Размеры: 500х500х500mm	10
М-18		Теннисный стол. Размеры: 1860х1050х760mm	2
М-19		Стул	8
М-20		Стол. Размеры: 3200х1500х750mm	1
М-21		Стол круглый. Размеры: 800х800х750h	5
М-22		Стул	7

Спецификация мебели			
Поз.	Изображение	Описание	Кол-во
М-23		Диван. Размеры: 1070х650х420h	3
М-24		Стул барный	6
М-25		Многофункциональная шведская стенка с турником, брусьями и скамьей	1
М-26		Многофункциональный силовой тренажер	1
М-27		Беговая дорожка	1
М-28		Силовой тренажер Клинбер	1
М-29		Боксерская груша	1

План расстановки мебели

Примечания

1. Данный лист смотреть совместно с альбомом визуализации.
2. Необходимо учитывать возможные погрешности в проектных и реальных размерах.
3. Перед изготовлением мебели необходимо уточнить фактические размеры.
4. Высотные отметки даны от уровня чистого пола 0.000.
5. Количество элементов спецификации даны без запаса.

Изм. Ном.

Описание

Подпись

Наименование проекта

Дизайн проект - АИ

Номер проекта

Дизайн проект - АИ

03.07.2026
12:50:17

Масштаб

1 : 100

Номер листа

10